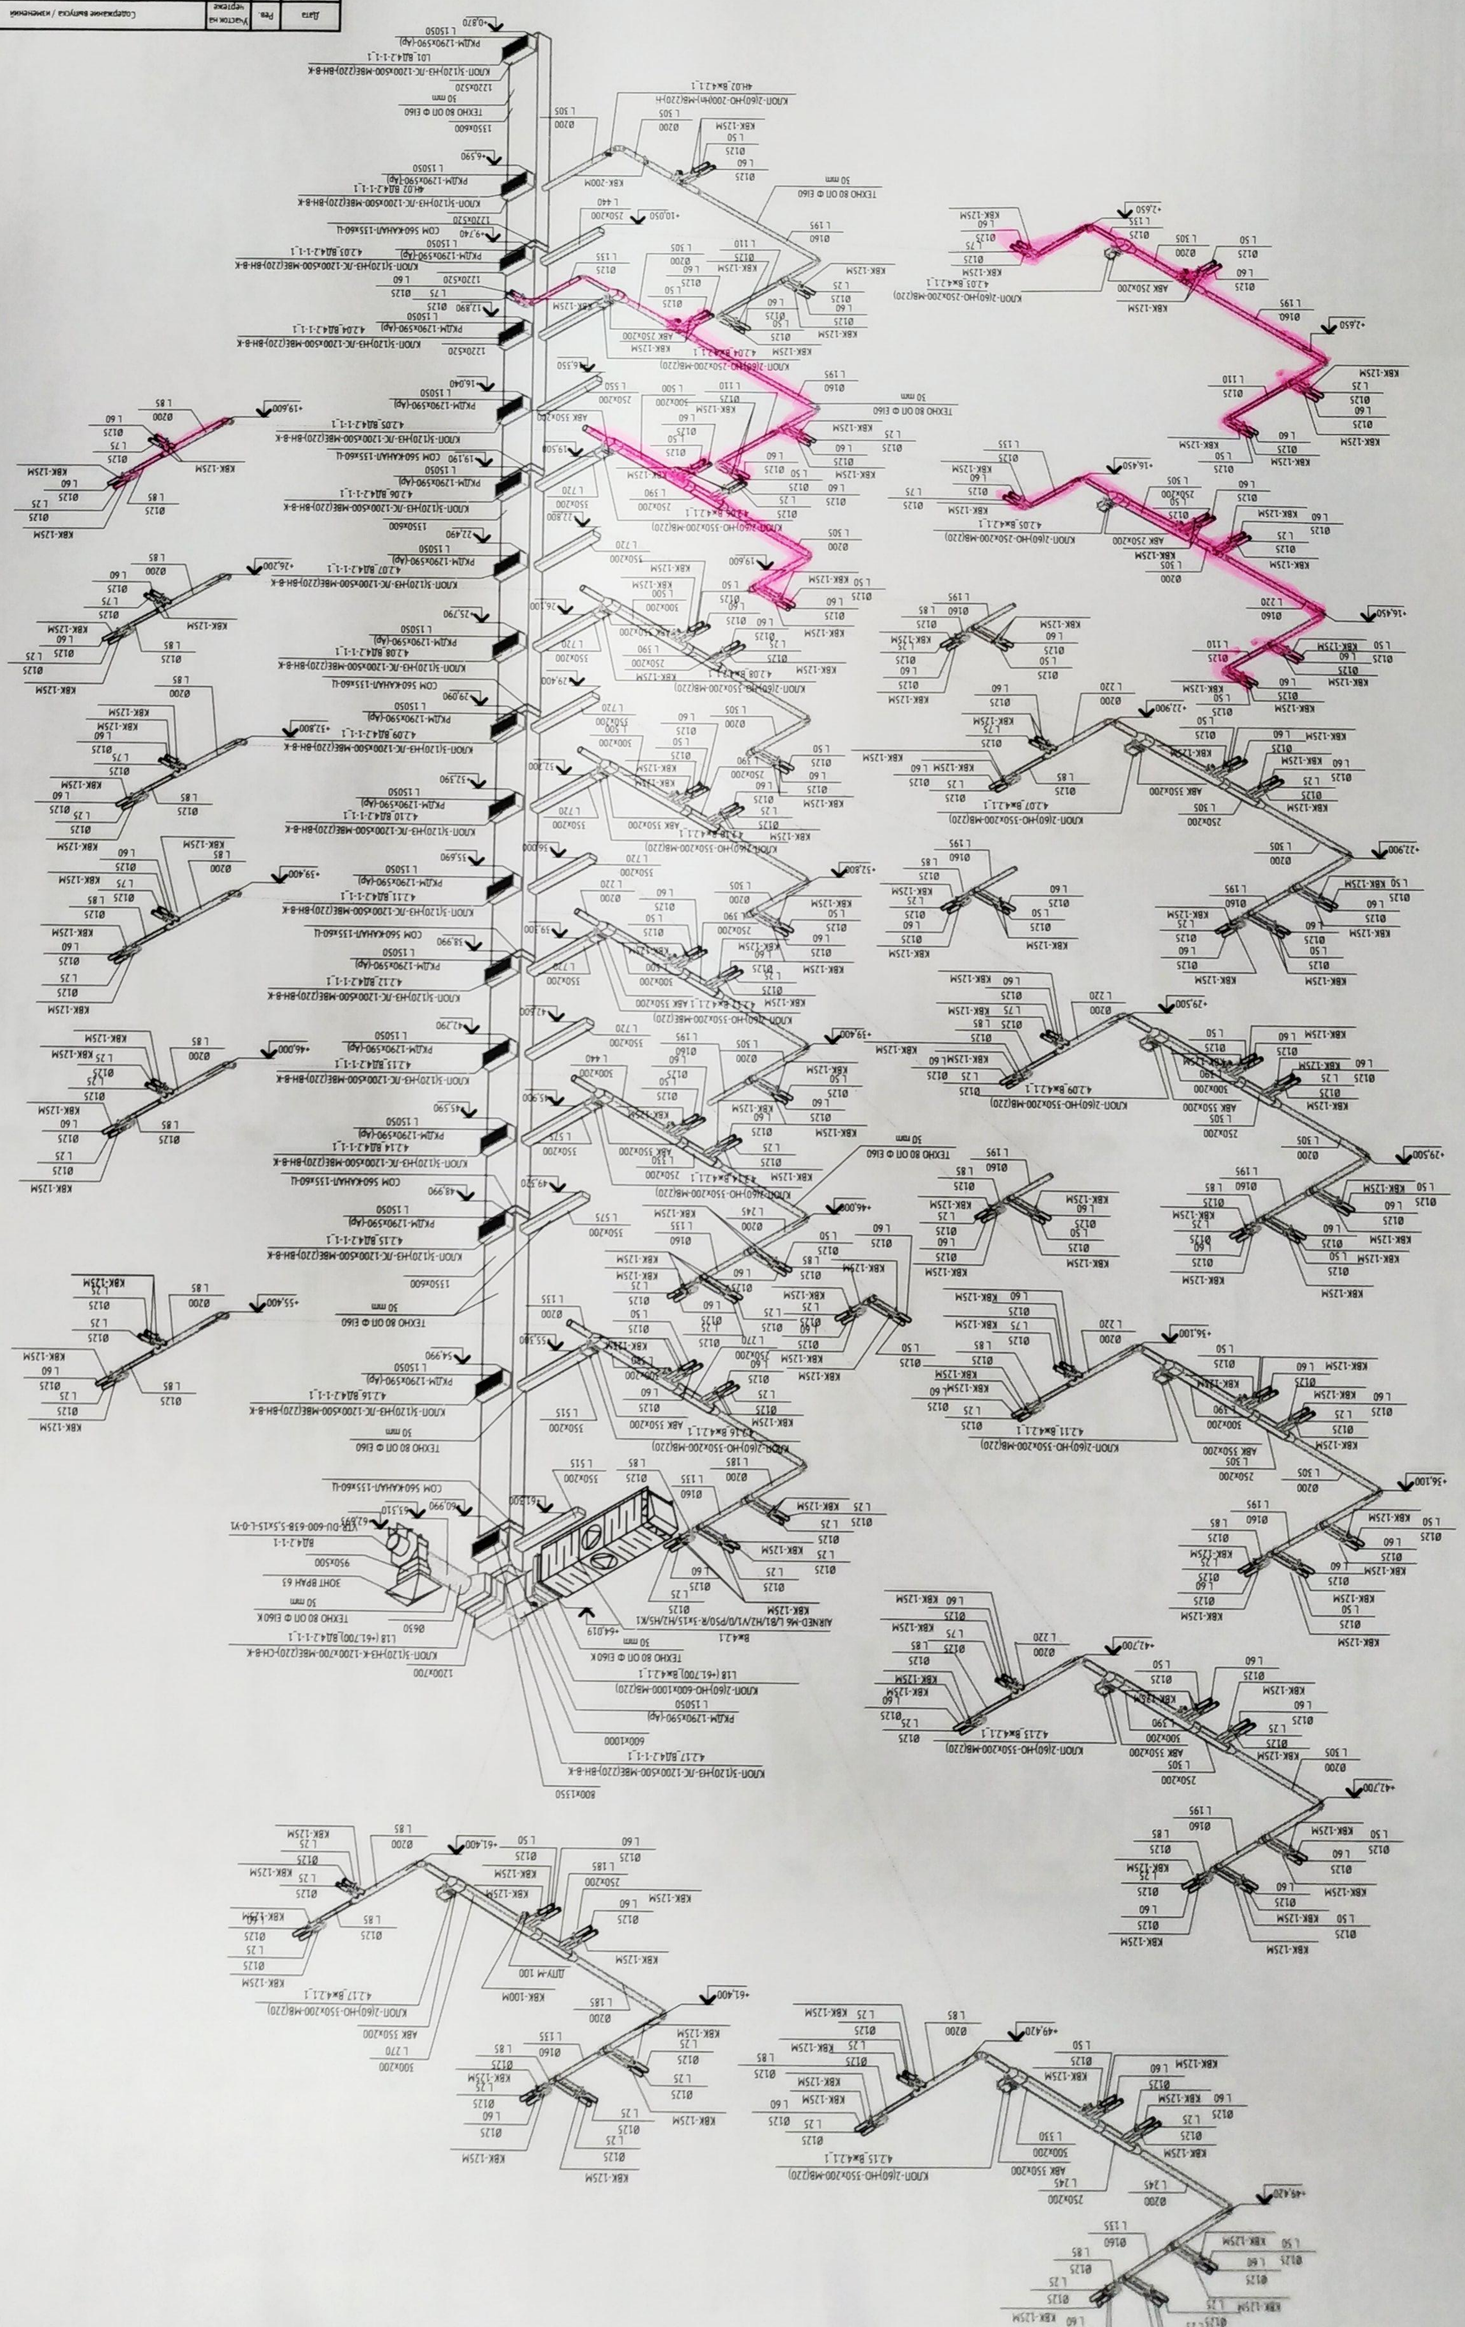

Изм.	Кол.уч.	Лист	N док.	Подпись	Дата
Разработал					03.20
Проверил					
Пр. примен.					
Пр. отдела					
Н. контр.					
ГИП					

1097-42/45-ОВ1

2-й этап строительства многофункционального жилого комплекса, расположенного по адресу: г. Москва, ЮАО, Нагатинская пойма, Проектируемый проезд 4062 вл 6

Вентиляция и кондиционирование воздуха. Противопожарные вентиляция. Корпус 4.2 и корпус 4.5

Стадия	Лист	Листов
Р	16	

ООО Проектное бюро АЛЕКС

Система СВ4.2-1-1.8А-4.2.1

Изм.	Кол.уч.	Лист	N док.	Подпись	Дата
Разработал					
Проверил					
Пр. примен.					
Пр. отдела					
Н. контр.					
ГИП					

Дата	Изм.	Участок на чертеже	Содержание внесенных / измененных	Подпись
06.20	С		42/45-ОВ1 - Корректировка рабочей документации	X
12.03.20	А		42/45-ОВ1 - Внутренние рабочие документации	X

Согласовано

Взам. инв. №

Подпись и дата

Инв. № подл.

Примечания

1. Данный чертеж нужно совместно с остальными листами проекта.
2. Все присоединения с противопожарными преградами должны быть заделаны в соответствии с проектом.
3. Размеры фланцев соединяют с размерами воздуховодов, на которые устанавливаются клапаны, если не указано иное.
4. Стенки воздуховодов дана без учета изоляции.
5. На схемах показана система уровня пола приямочтиамах и оси крупных воздуховодов.
6. Адресная система автоматизированного пожаротушения с уровнем 0,007 в стороны сада.